


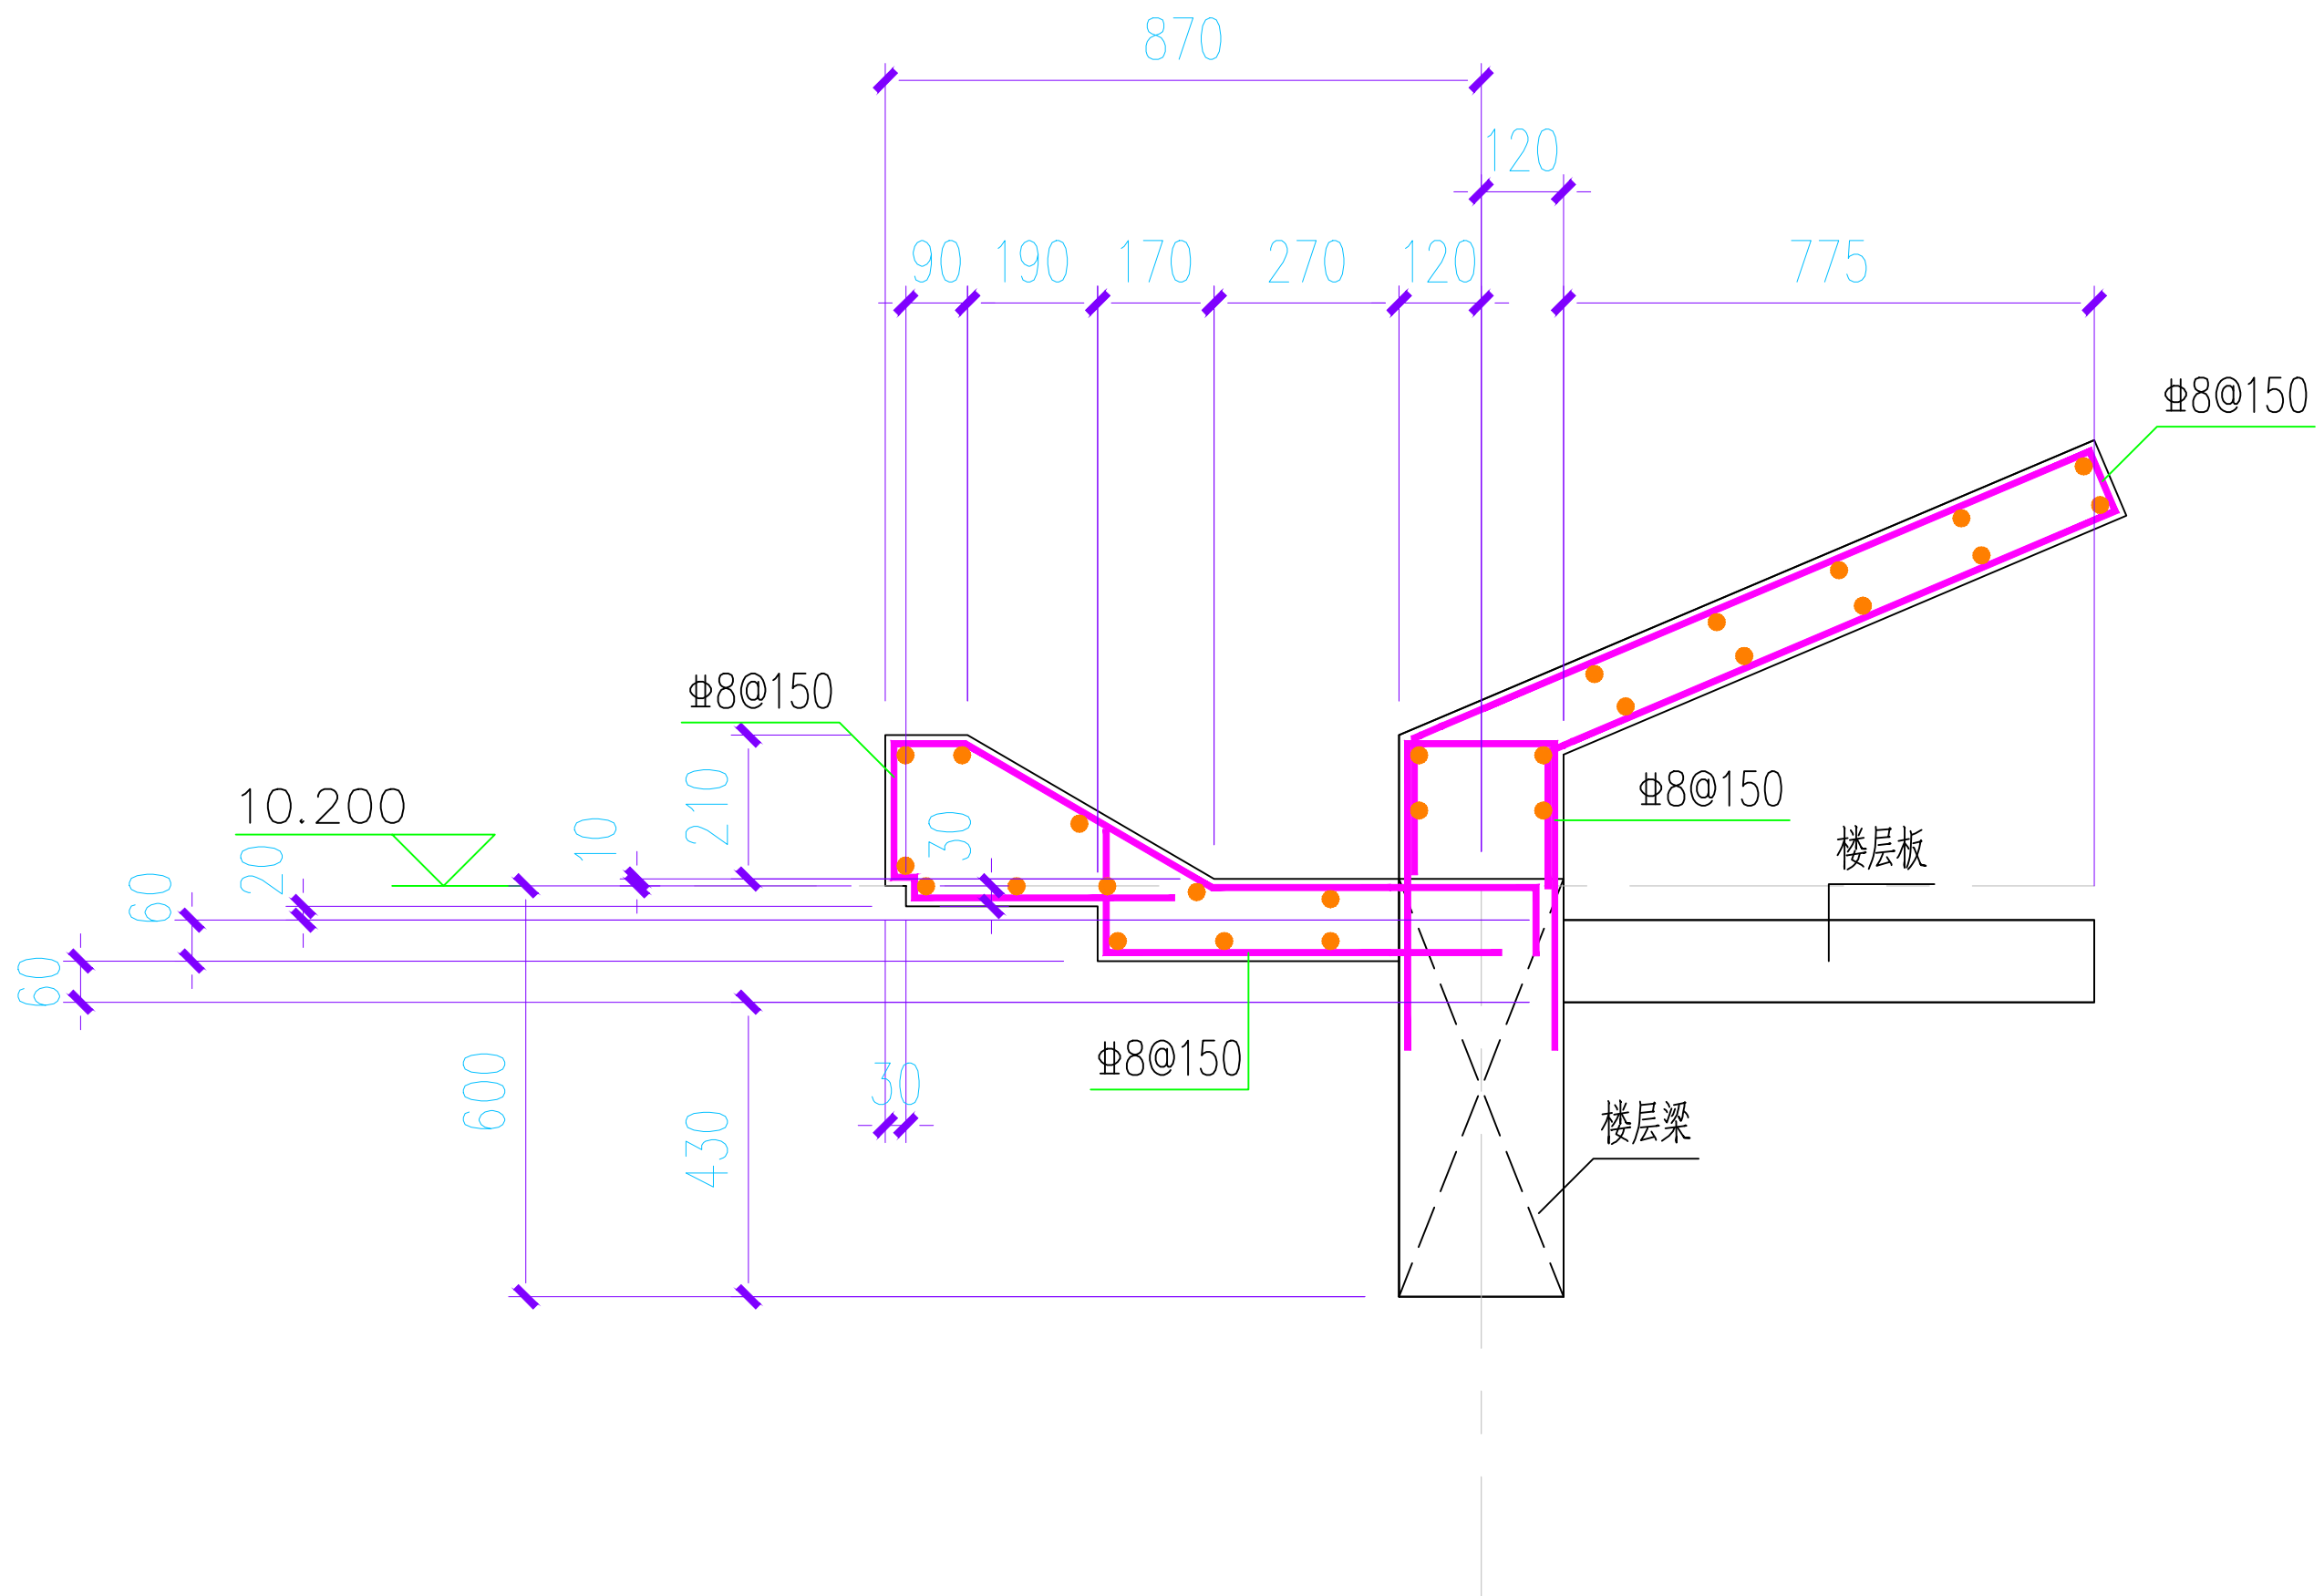

# 1 檐口大样图

未注明的分布点筋均为 $\Phi 8$